


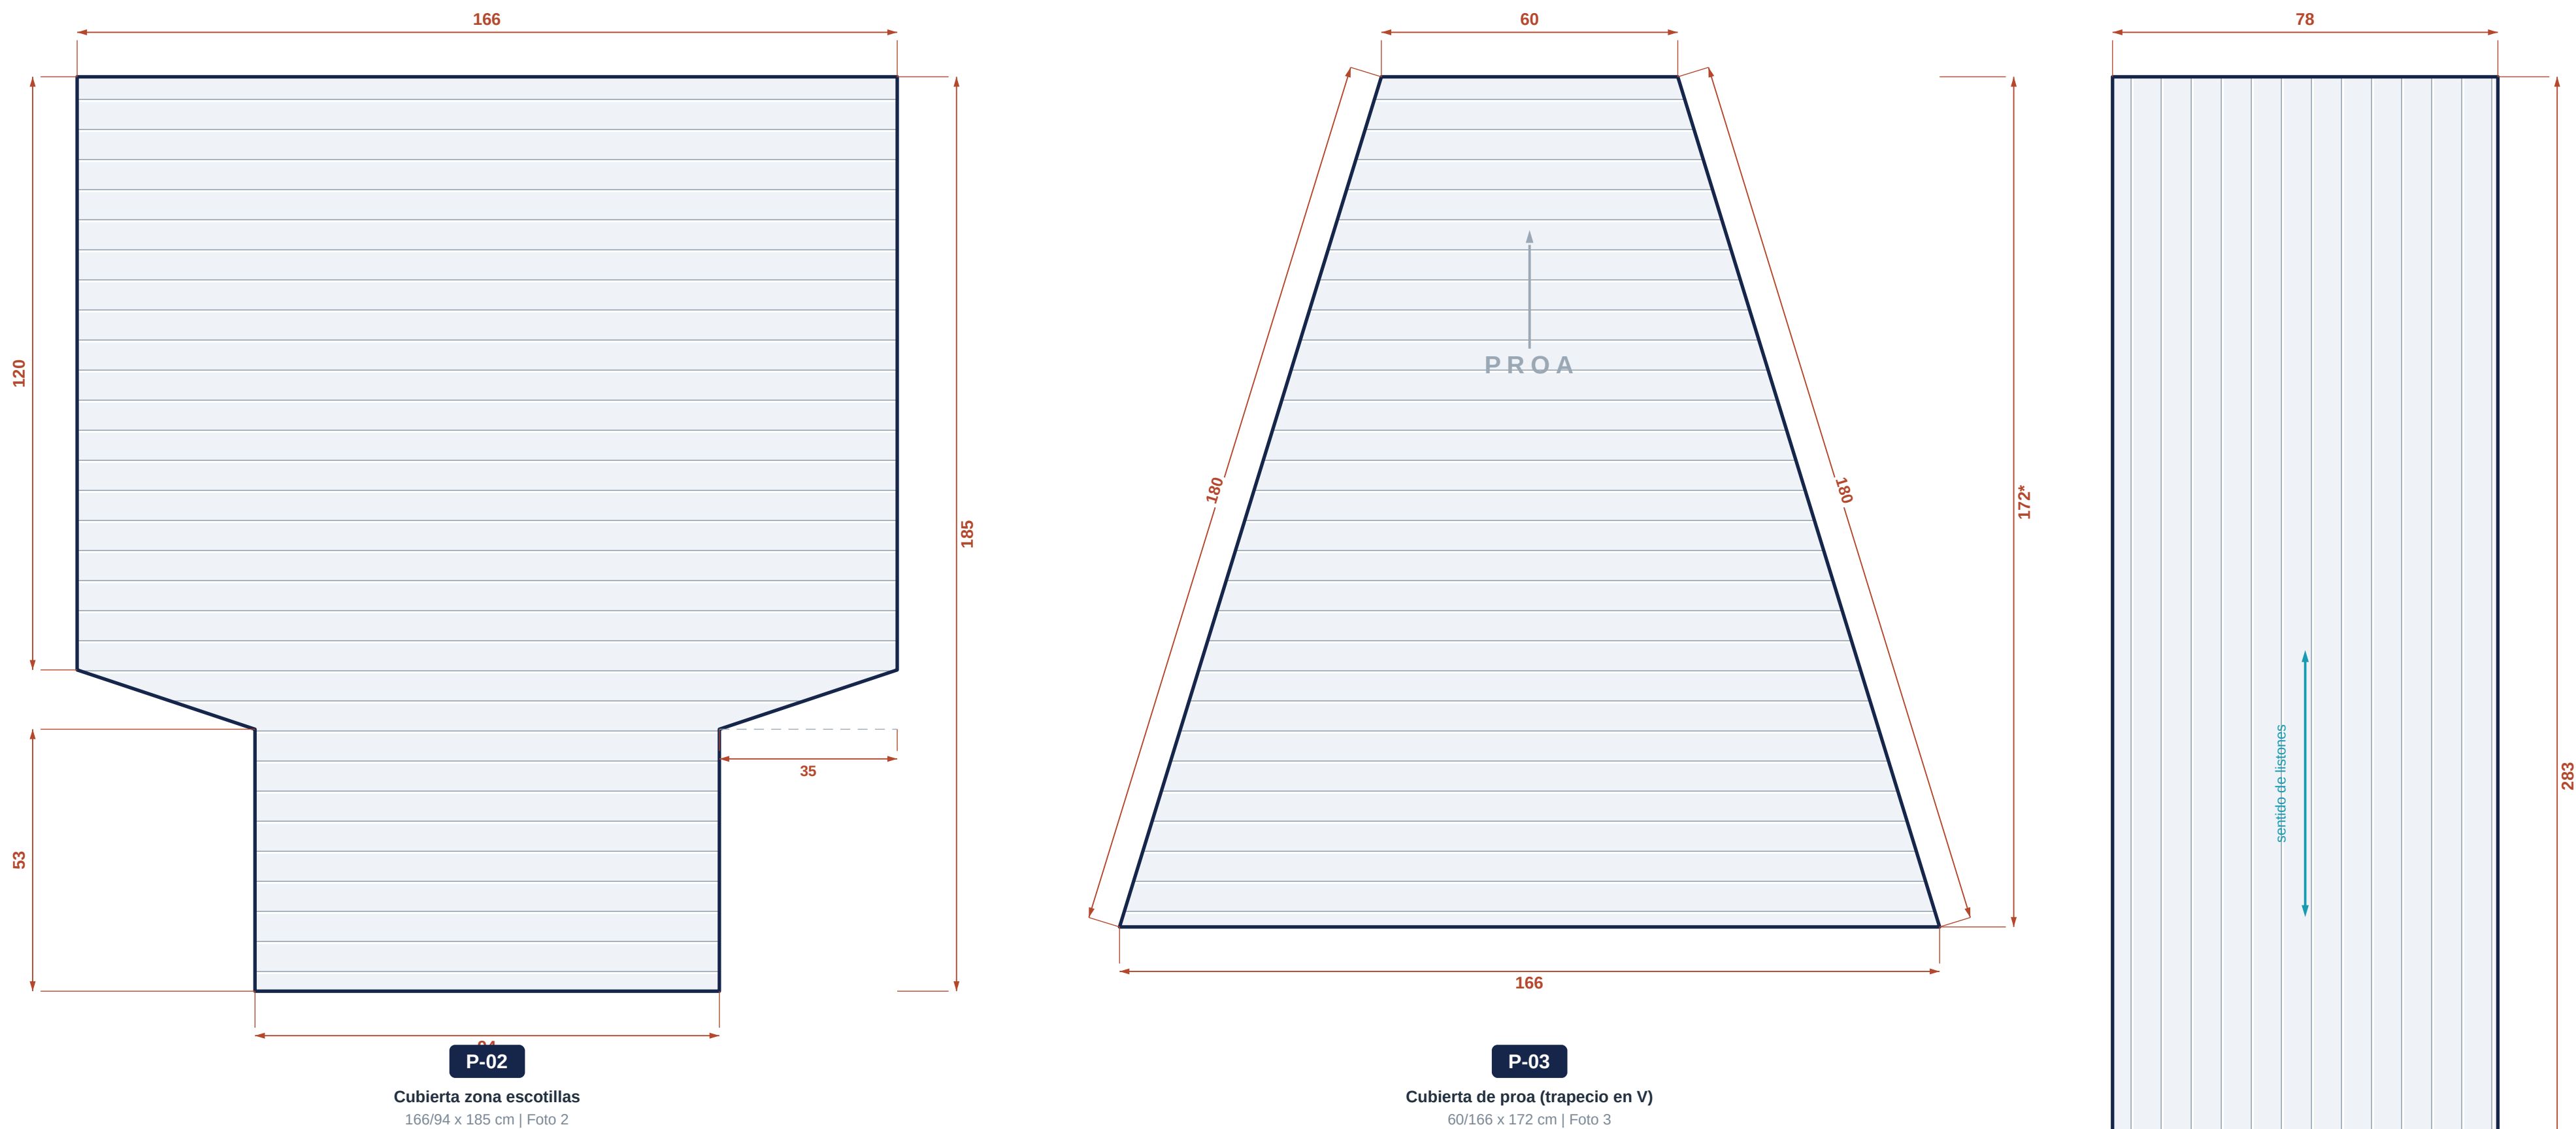

RELACION DE PIEZAS

REF.	DESCRIPCION	MEDIDAS (cm)	CANT.	AREA (m²)
P-01	Pasillo central de cubierta	78 x 283	1	2,207
P-02	Cubierta zona escotillas (acceso escalera)	166/94 x 185	1	2,646
P-03	Cubierta de proa - trapecio en V	60/166 x 172	1	1,944
P-04	Panel lateral A - banda babor	45 x 103	1	0,464
P-05	Panel lateral B - banda babor	70 x 103	1	0,721
P-06	Panel lateral C - banda estribor	70 x 103	1	0,721
P-07	Panel lateral D - banda estribor	40 x 103	1	0,412
P-08	Escalon superior	58 x 28	1	0,162
P-09	Escalon inferior	58 x 28	1	0,162
TOTAL			9	9,440

Superficie neta, sin solapes ni despunte. Prever ~10-15 % de merma de corte.

NOTAS

- Todas las cotas en centímetros, tomadas en obra sobre la embarcacion. Verificar in situ antes de cortar; plantillar las piezas con contornos irregulares (P-02 y P-03) sobre el propio soporte.
- Sólo se representan las piezas marcadas en VERDE en las fotos. Las zonas marcadas en amarillo o tachadas quedan expresamente excluidas.
- P-01 y P-04 a P-09: en las fotos el contorno aparece trapecial por efecto de perspectiva; se interpretan como rectángulos según las dos cotas anotadas en cada uno.
- P-02: el alto total de 185 se descompone en 120 (tramo recto) + 12 (chafflan) + 53 (tramo recto). El retranqueo lateral anotado de 35 se resuelve con 36 por lado para cerrar 166 - 72 = 94 en la base.
- (*) P-03: la altura 172 es calculada a partir de las bases 60 y 166 y los lados de 180 (no fue medida directamente en obra).
- P-08 y P-09 son dos escalones idénticos de 58 x 28.
- Holgura recomendada de montaje: 3 a 5 mm en todo el perímetro.
- Sentido del listonado: longitudinal a la eslora salvo indicación contraria.


ESCALA GRAFICA 1:10



LEYENDA

- Pieza a fabricar (marcada en VERDE en las fotos)
- Zona descartada (AMARILLO / tachada) - NO se fabrica
- Cota tomada en obra (cm)
- Sentido sugerido del listonado

FOTOS DE REFERENCIA (levantamiento en obra)

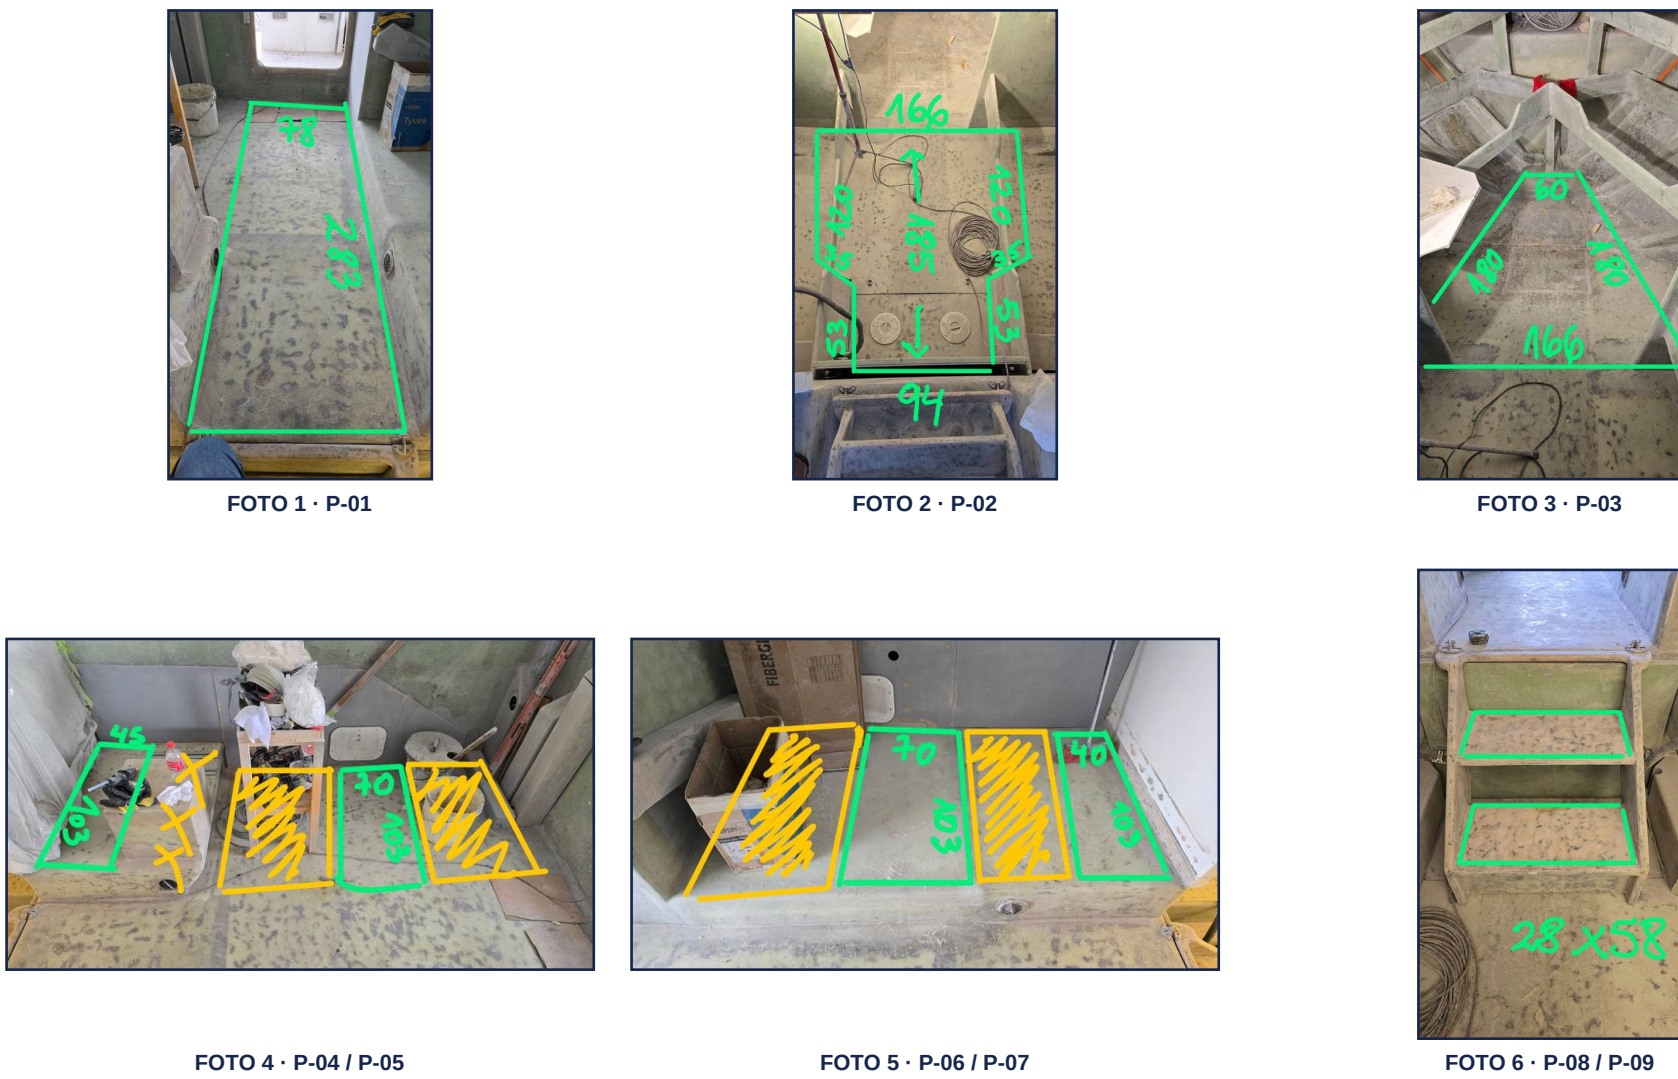

VERIFICACION DE MEDIDAS EN OBRA (a rellenar antes del corte)

REF.	MEDIDA DE PLANO (cm)	MEDIDA VERIFICADA (cm)	CONFORME	
P-01	78 x 283		☐ SI	☐ NO
P-02	166/94 x 185		☐ SI	☐ NO
P-03	60/166 x 172		☐ SI	☐ NO
P-04	45 x 103		☐ SI	☐ NO
P-05	70 x 103		☐ SI	☐ NO
P-06	70 x 103		☐ SI	☐ NO
P-07	40 x 103		☐ SI	☐ NO
P-08	58 x 28		☐ SI	☐ NO
P-09	58 x 28		☐ SI	☐ NO

CLIENTE	—
EMBARCACION / OBRA	—
CONTENIDO	Despiece de paneles de cubierta
ESCALA	1:10 (A1)
UNIDADES	centímetros
FECHA	03 / 08 / 2026
REV.	00
HOJA	1 de 1